


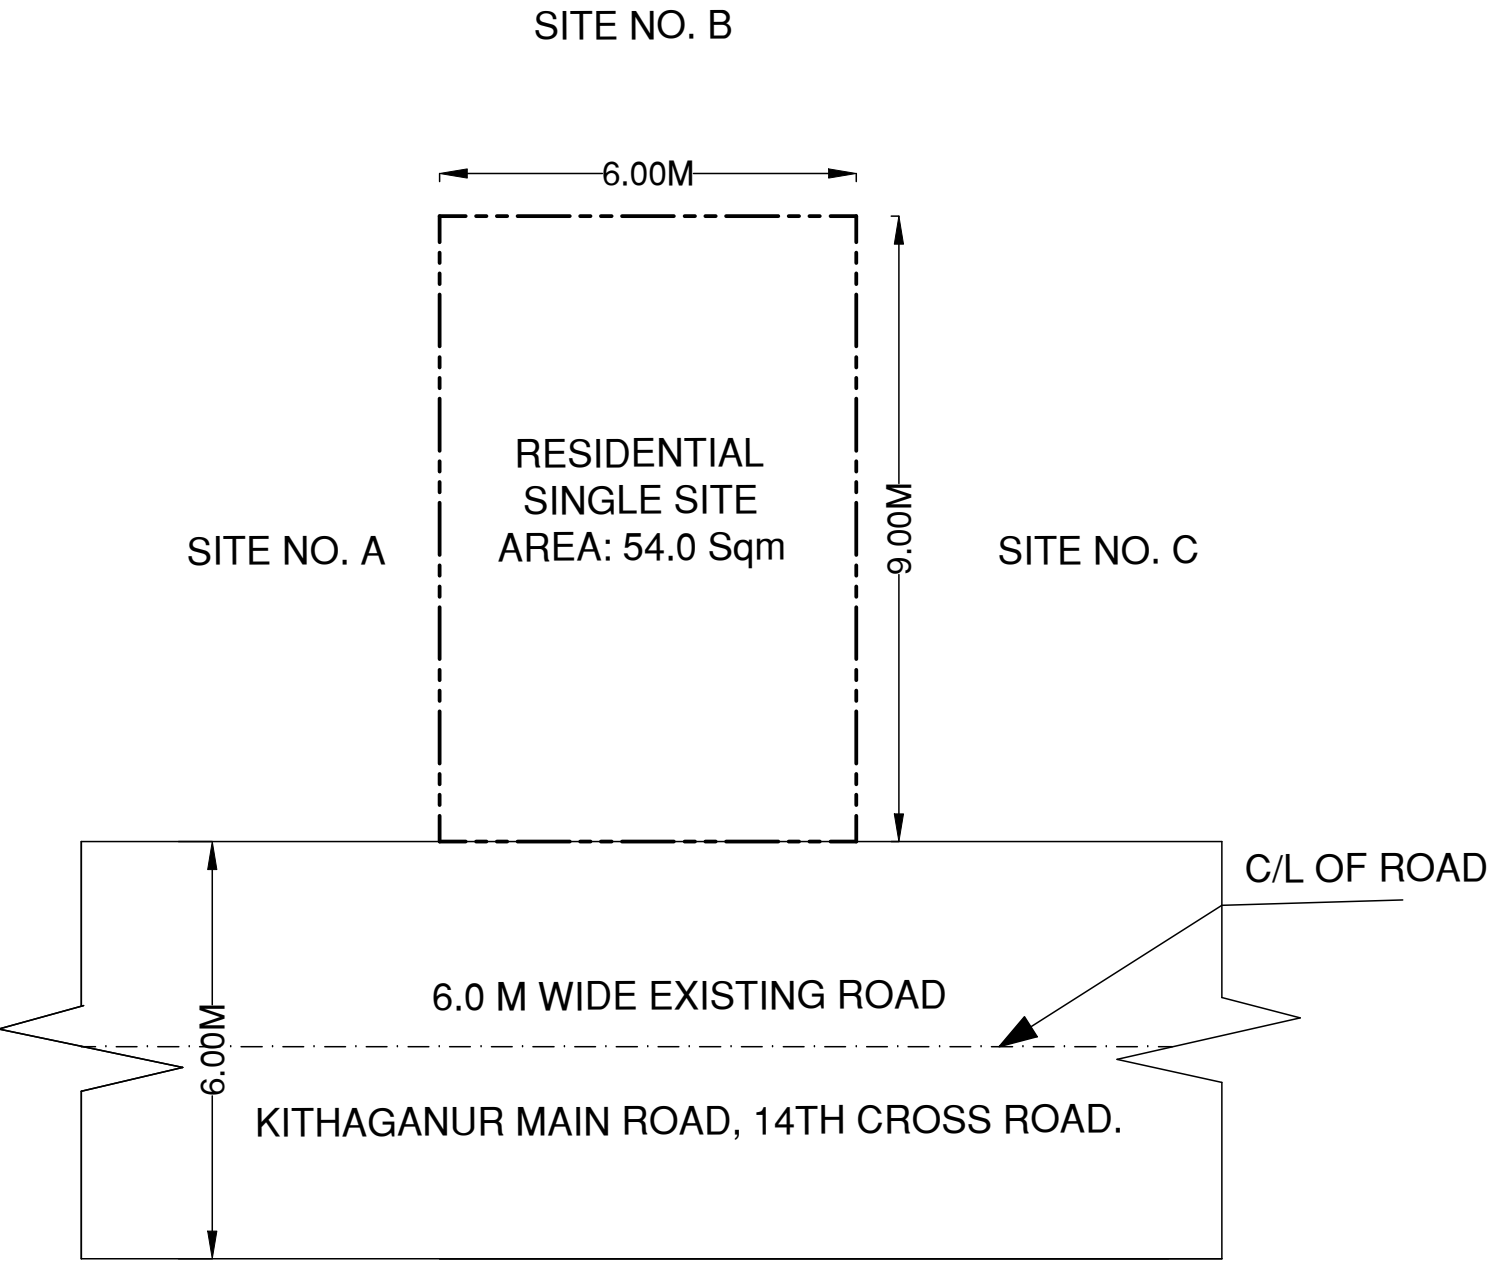

SAMPLE FORMAT 6.0.0M x9.0 M SITE RESIDENTIAL SINGLE PLOT LAYOUT PLAN

ADLR SKETCH SHOWING THE LOCATION OF THE PROPOSED SITE WITHIN THE SURVEY NUMBER.

KEY PLAN					CONVERSION ORDER DETAILS				
GENERAL CONDITIONS OF APPROVAL					LAND USE ANALYSIS			LEGEND	
1. The single plot layout plan is approved based on the survey sketch certified by the Assistant Director of Land records. 2. Building construction shall be undertaken only after obtaining approval for the building plan from the city corporation as per the approved single site layout plan. 3. The existing width of road abutting the site in question is marked in the plan. At the time of building plan approval the authority approving the building plan shall allow the maximum FAR permissible considering the minimum width of the road at any stretch towards any one side which shall join a road of equal or higher width. 4. The owner shall provide drinking water, waste water discharge system, solid waste management system and drainage system for the site in question. During the building plan approval the owner shall submit a design to implement the rain water harvesting to collect the rain water from the entire site area. 5. Approval of single site layout plan shall not be a document to claim title to the property. In case of pending cases under the Land Reforms Act/Section 136(3) of the Land Revenue Act, 1964, approval of single site layout plan shall be subject to final order. The applicant shall be bound by the final order of the court in this regard and in no case the fees paid for the approval of the single site layout plan will be refunded. 6. If it is found that the land proposed by the applicant includes any land belonging to the Government or any other private land, in such a case, the Authority reserves the rights to modify the single site layout plan or to withdraw the plan. 7. If it is proved that the applicant has provided any false documents or forged documents for the plan sanction, the plan sanction shall stand canceled automatically. 8. The applicant shall be bound to all subsequent orders and the decision relating to payment of fees as required by the Authority. 9. Adequate provisions shall be made to segregate wet waste, dry waste and plastics. Area should be reserved for composting of wet waste, dry waste etc. 10. No Objection Certificates/Approvals for the building plan should be obtained from the competent authorities prior to construction of building on the approved single site. 11. Sewage shall not be discharged into open spaces/vacant areas but should be reused for gardening, cleaning of common areas and various other uses. 12. If the owner wishes to modify the single site layout approval to multi-plot residential layout, the owner shall submit a request to the Greater Bengaluru Authority and obtain approval for the multi-plot residential layout plan as per the zoning regulations. 13. One tree for every 240.0 sq.m. of the total floor area shall be planted and nurtured at the site in question. 14. Prior permission should be obtained from the competent authority before constructing a culvert on the storm water drain between the land in question and the existing road attached to it if any. 15. To abide by such other conditions as may be imposed by the Authority from time to time.					SL. No	PARTICULARS	AREA IN Sqm.	%	- - - - - PROPERTY BOUNDARY LINE
					1	RESIDENTIAL AREA	54.0	100.00	
2	TOTAL SITE AREA	54.0	100.00						
OWNER SIGNATURE					ARCHITECT SIGNATURE & REGISTRATION DETAILS				
DRAWING TITLE									
PLAN SHOWING THE RESIDENTIAL SINGLE SITE LAYOUT FOR THE PROPERTY SITUATED IN SY.NO.****, **** VILLAGE, **** TALUK, BEARING KHATA/PID NO.***** , ***** ROAD , WARD NO. ***** , ***** CONSTITUENCY , BENGALURU ***** CORPORATION , BENGALURU.									
SANCTIONING AUTHORITY					SCALE 1:100				


NOTE

1. The single plot plan is issued under The Provision of section 17 of KTCP Act 1961

2. The applicant has Remitted Fees of Rs.***** vide challan No. ***** Dated : **.*.****

3. The applicant has to abide by the conditions imposed in the single plot plan approval order

4. This single plot plan issued vide number ***/**/***-***** dated : **.*.****

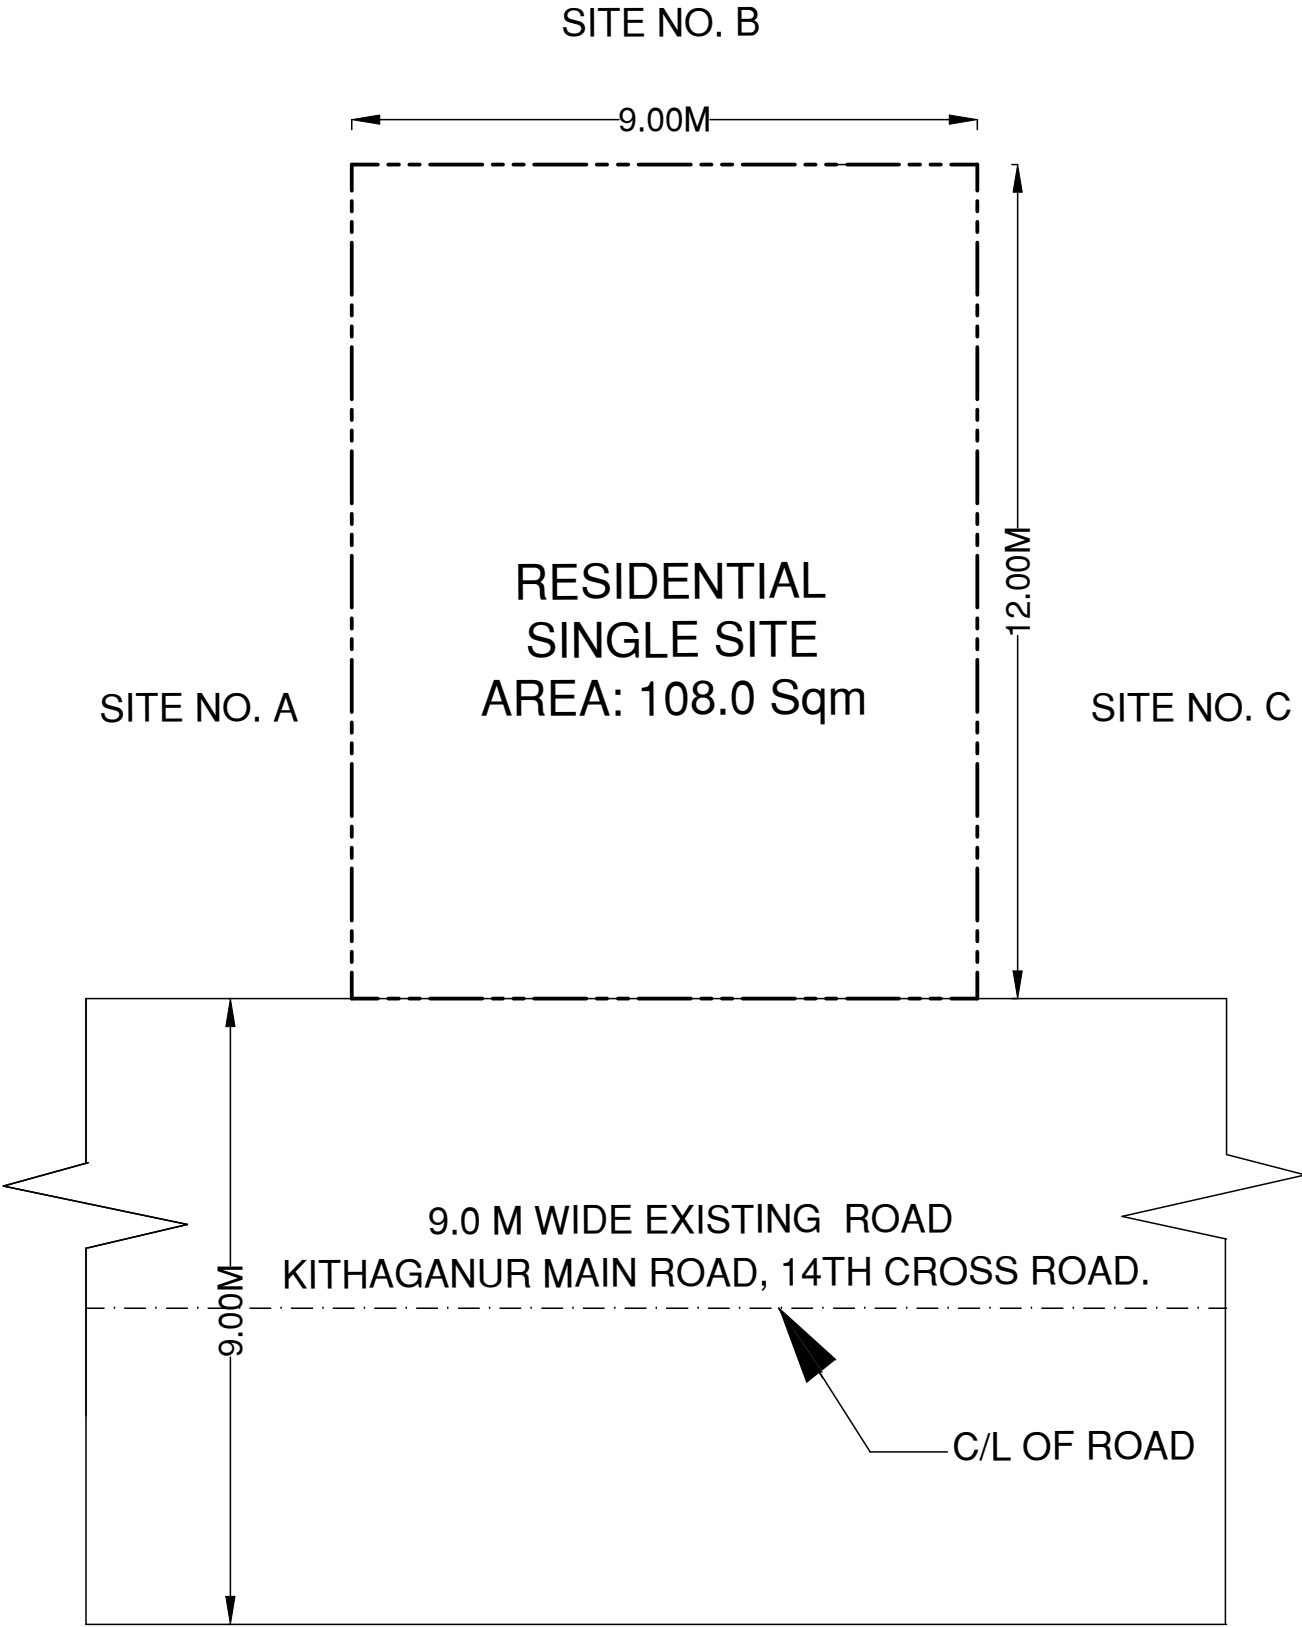

SAMPLE FORMAT 9.0.0M x12.0 M SITE RESIDENTIAL SINGLE PLOT LAYOUT PLAN

ADLR SKETCH SHOWING THE LOCATION OF THE PROPOSED SITE WITHIN THE SURVEY NUMBER.

KEY PLAN

CONVERSION ORDER DETAILS

LAND USE ANALYSIS				LEGEND
SL. No	PARTICULARS	AREA IN Sqm.	%	
1	RESIDENTIAL AREA	108.0	100.00	--- -- PROPERTY BOUNDARY LINE //// ROAD WIDENING AREA
2	TOTAL SITE AREA	108.0	100.00	

OWNER SIGNATURE

ARCHITECT SIGNATURE & REGISTRATION DETAILS

DRAWING TITLE

PLAN SHOWING THE RESIDENTIAL SINGLE SITE LAYOUT FOR THE PROPERTY SITUATED IN SY.NO.****, **** VILLAGE, **** TALUK, BEARING KHATA/PID NO.***** , ***** ROAD , WARD NO. ***** , ***** CONSTITUENCY , BENGALURU ***** CORPORATION , BENGALURU.

N

All Dimensions in metres.

SCALE 1:100

SANCTIONING AUTHORITY

GENERAL CONDITIONS OF APPROVAL

1. The single plot layout plan is approved based on the survey sketch certified by the Assistant Director of Land records.

2. Building construction shall be undertaken only after obtaining approval for the building plan from the city corporation as per the approved single site layout plan.

3. The existing width of road abutting the site in question is marked in the plan. At the time of building plan approval the authority approving the building plan shall allow the maximum FAR permissible considering the minimum width of the road at any stretch towards any one side which shall join a road of equal or higher width.

4. The owner shall provide drinking water, waste water discharge system, solid waste management system and drainage system for the site in question. During the building plan approval the owner shall submit a design to implement the rain water harvesting to collect the rain water from the entire site area.

5. Approval of single site layout plan shall not be a document to claim title to the property. In case of pending cases under the Land Reforms Act/Section 136(3) of the Land Revenue Act, 1964, approval of single site layout plan shall be subject to final order. The applicant shall be bound by the final order of the court in this regard and in no case the fees paid for the approval of the single site layout plan will be refunded.

6. If it is found that the land proposed by the applicant includes any land belonging to the Government or any other private land, in such a case, the Authority reserves the rights to modify the single site layout plan or to withdraw the plan.

7. If it is proved that the applicant has provided any false documents or forged documents for the plan sanction, the plan sanction shall stand canceled automatically.

8. The applicant shall be bound to all subsequent orders and the decision relating to payment of fees as required by the Authority.

9. Adequate provisions shall be made to segregate wet waste, dry waste and plastics. Area should be reserved for composting of wet waste, dry waste etc.

10. No Objection Certificates/Approvals for the building plan should be obtained from the competent authorities prior to construction of building on the approved single site.

11. Sewage shall not be discharged into open spaces/vacant areas but should be reused for gardening, cleaning of common areas and various other uses.

12. If the owner wishes to modify the single site layout approval to multi-plot residential layout, the owner shall submit a request to the Greater Bengaluru Authority and obtain approval for the multi-plot residential layout plan as per the zoning regulations.

13. One tree for every 240.0 sq.m. of the total floor area shall be planted and nurtured at the site in question.

14. Prior permission should be obtained from the competent authority before constructing a culvert on the storm water drain between the land in question and the existing road attached to it if any.

15. To abide by such other conditions as may be imposed by the Authority from time to time.


NOTE

1. The single plot plan is issued under The Provision of section 17 of KTCP Act 1961

2. The applicant has Remitted Fees of Rs.***** vide challan No. ***** Dated : **..****

3. The applicant has to abide by the conditions imposed in the single plot plan approval order

4. This single plot plan issued vide number **/**/**-***** dated : **..****

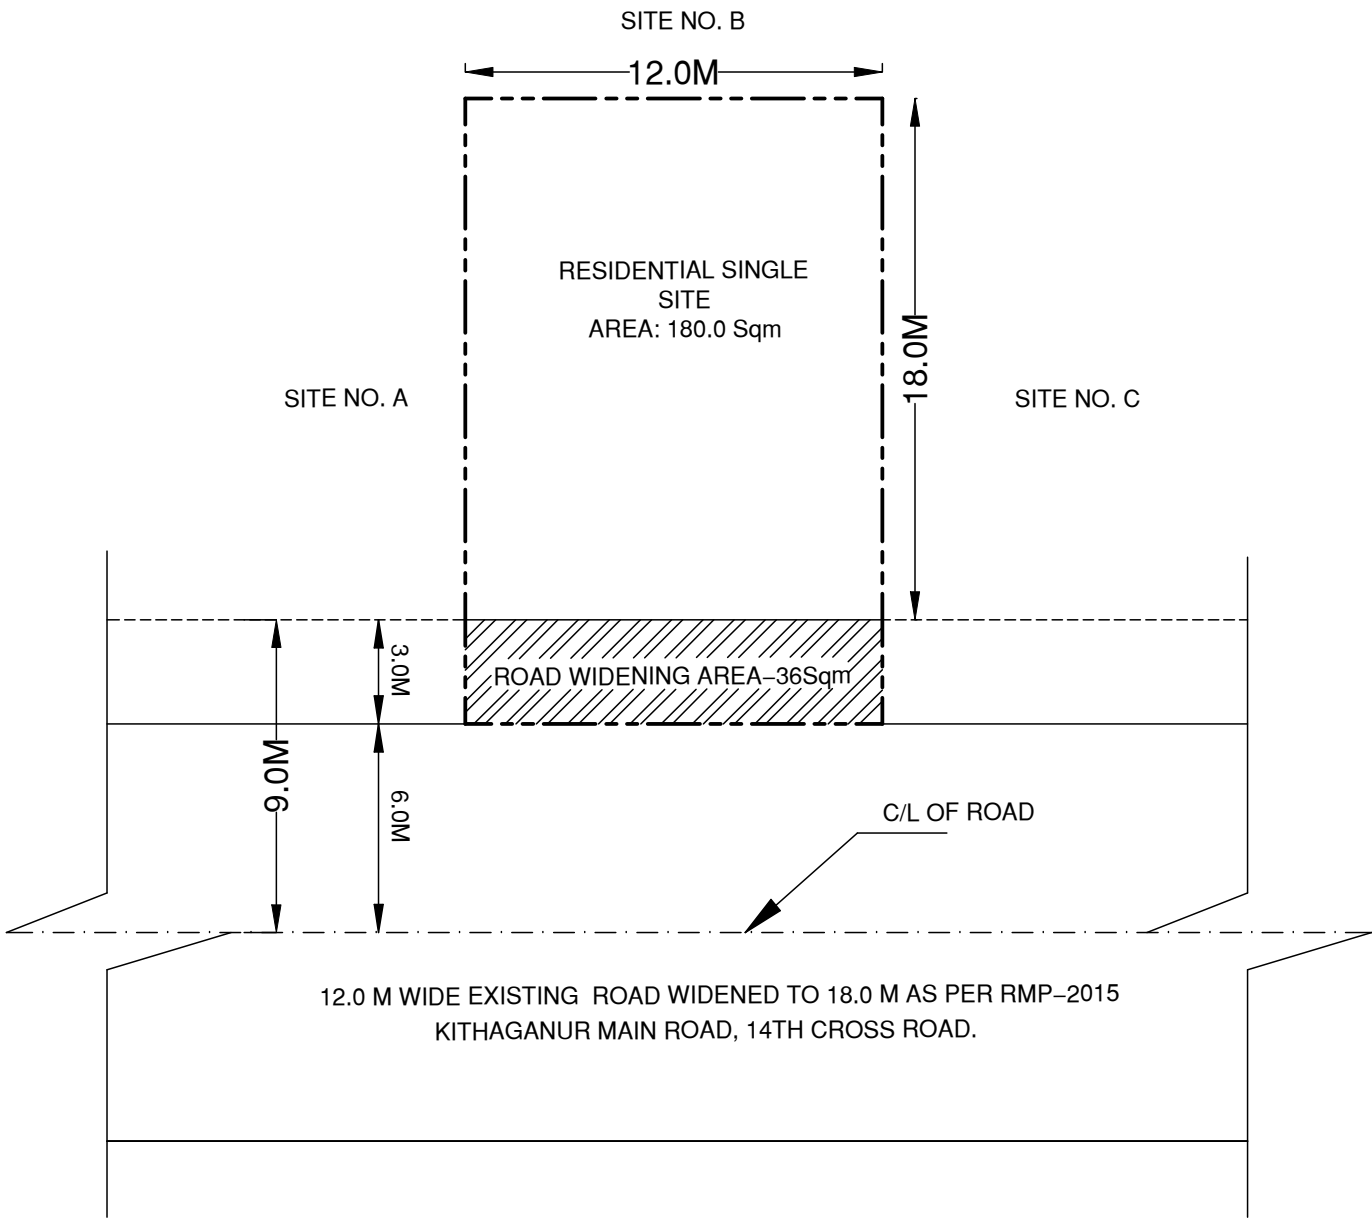

SAMPLE FORMAT 12.0M x18.0 M SITE RESIDENTIAL SINGLE PLOT LAYOUT PLAN

ADLR SKETCH SHOWING THE LOCATION OF THE PROPOSED SITE WITHIN THE SURVEY NUMBER.

KEY PLAN

CONVERSION ORDER DETAILS

GENERAL CONDITIONS OF APPROVAL

1. The single plot layout plan is approved based on the survey sketch certified by the Assistant Director of Land records.

2. Building construction shall be undertaken only after obtaining approval for the building plan from the city corporation as per the approved single site layout plan.

3. The existing width of road abutting the site in question is marked in the plan. At the time of building plan approval the authority approving the building plan shall allow the maximum FAR permissible considering the minimum width of the road at any stretch towards any one side which shall join a road of equal or higher width.

4. The owner shall provide drinking water, waste water discharge system, solid waste management system and drainage system for the site in question. During the building plan approval the owner shall submit a design to implement the rain water harvesting to collect the rain water from the entire site area.

5. Approval of single site layout plan shall not be a document to claim title to the property. In case of pending cases under the Land Reforms Act/Section 136(3) of the Land Revenue Act, 1964, approval of single site layout plan shall be subject to final order. The applicant shall be bound by the final order of the court in this regard and in no case the fees paid for the approval of the single site layout plan will be refunded.

6. If it is found that the land proposed by the applicant includes any land belonging to the Government or any other private land, in such a case, the Authority reserves the rights to modify the single site layout plan or to withdraw the plan.

7. If it is proved that the applicant has provided any false documents or forged documents for the plan sanction, the plan sanction shall stand canceled automatically.

8. The applicant shall be bound to all subsequent orders and the decision relating to payment of fees as required by the Authority.

9. Adequate provisions shall be made to segregate wet waste, dry waste and plastics. Area should be reserved for composting of wet waste, dry waste etc.

10. No Objection Certificates/Approvals for the building plan should be obtained from the competent authorities prior to construction of building on the approved single site.

11. Sewage shall not be discharged into open spaces/vacant areas but should be reused for gardening, cleaning of common areas and various other uses.

12. If the owner wishes to modify the single site layout approval to multi-plot residential layout, the owner shall submit a request to the Greater Bengaluru Authority and obtain approval for the multi-plot residential layout plan as per the zoning regulations.

13. One tree for every 240.0 sq.m. of the total floor area shall be planted and nurtured at the site in question.

14. Prior permission should be obtained from the competent authority before constructing a culvert on the storm water drain between the land in question and the existing road attached to it if any.

15. To abide by such other conditions as may be imposed by the Authority from time to time.

NOTE

1. The single plot plan is issued under The Provision of section 17 of KTCP Act 1961

2. The applicant has Remitted Fees of Rs.***** vide challan No. ***** Dated : **.*.****

3. The applicant has to abide by the conditions imposed in the single plot plan approval order

4. This single plot plan issued vide number ***/**/***-***** dated : **.*.****

LAND USE ANALYSIS

LEGEND

SL. No	PARTICULARS	AREA IN Sqm.	%
1	RESIDENTIAL AREA	180.0	83.33
2	ROAD WIDENING AREA	36.0	16.67
3	TOTAL SITE AREA	216.0	100.00

OWNER SIGNATURE

ARCHITECT SIGNATURE & REGISTRATION DETAILS

DRAWING TITLE


PLAN SHOWING THE RESIDENTIAL SINGLE SITE LAYOUT FOR THE PROPERTY SITUATED IN SY.NO.****, **** VILLAGE, **** TALUK, BEARING KHATA/PID NO.***** , ***** ROAD , WARD NO. ***** , ***** CONSTITUENCY , BENGALURU ***** CORPORATION , BENGALURU.

SANCTIONING AUTHORITY


N

All Dimensions in metres.

SCALE 1:200

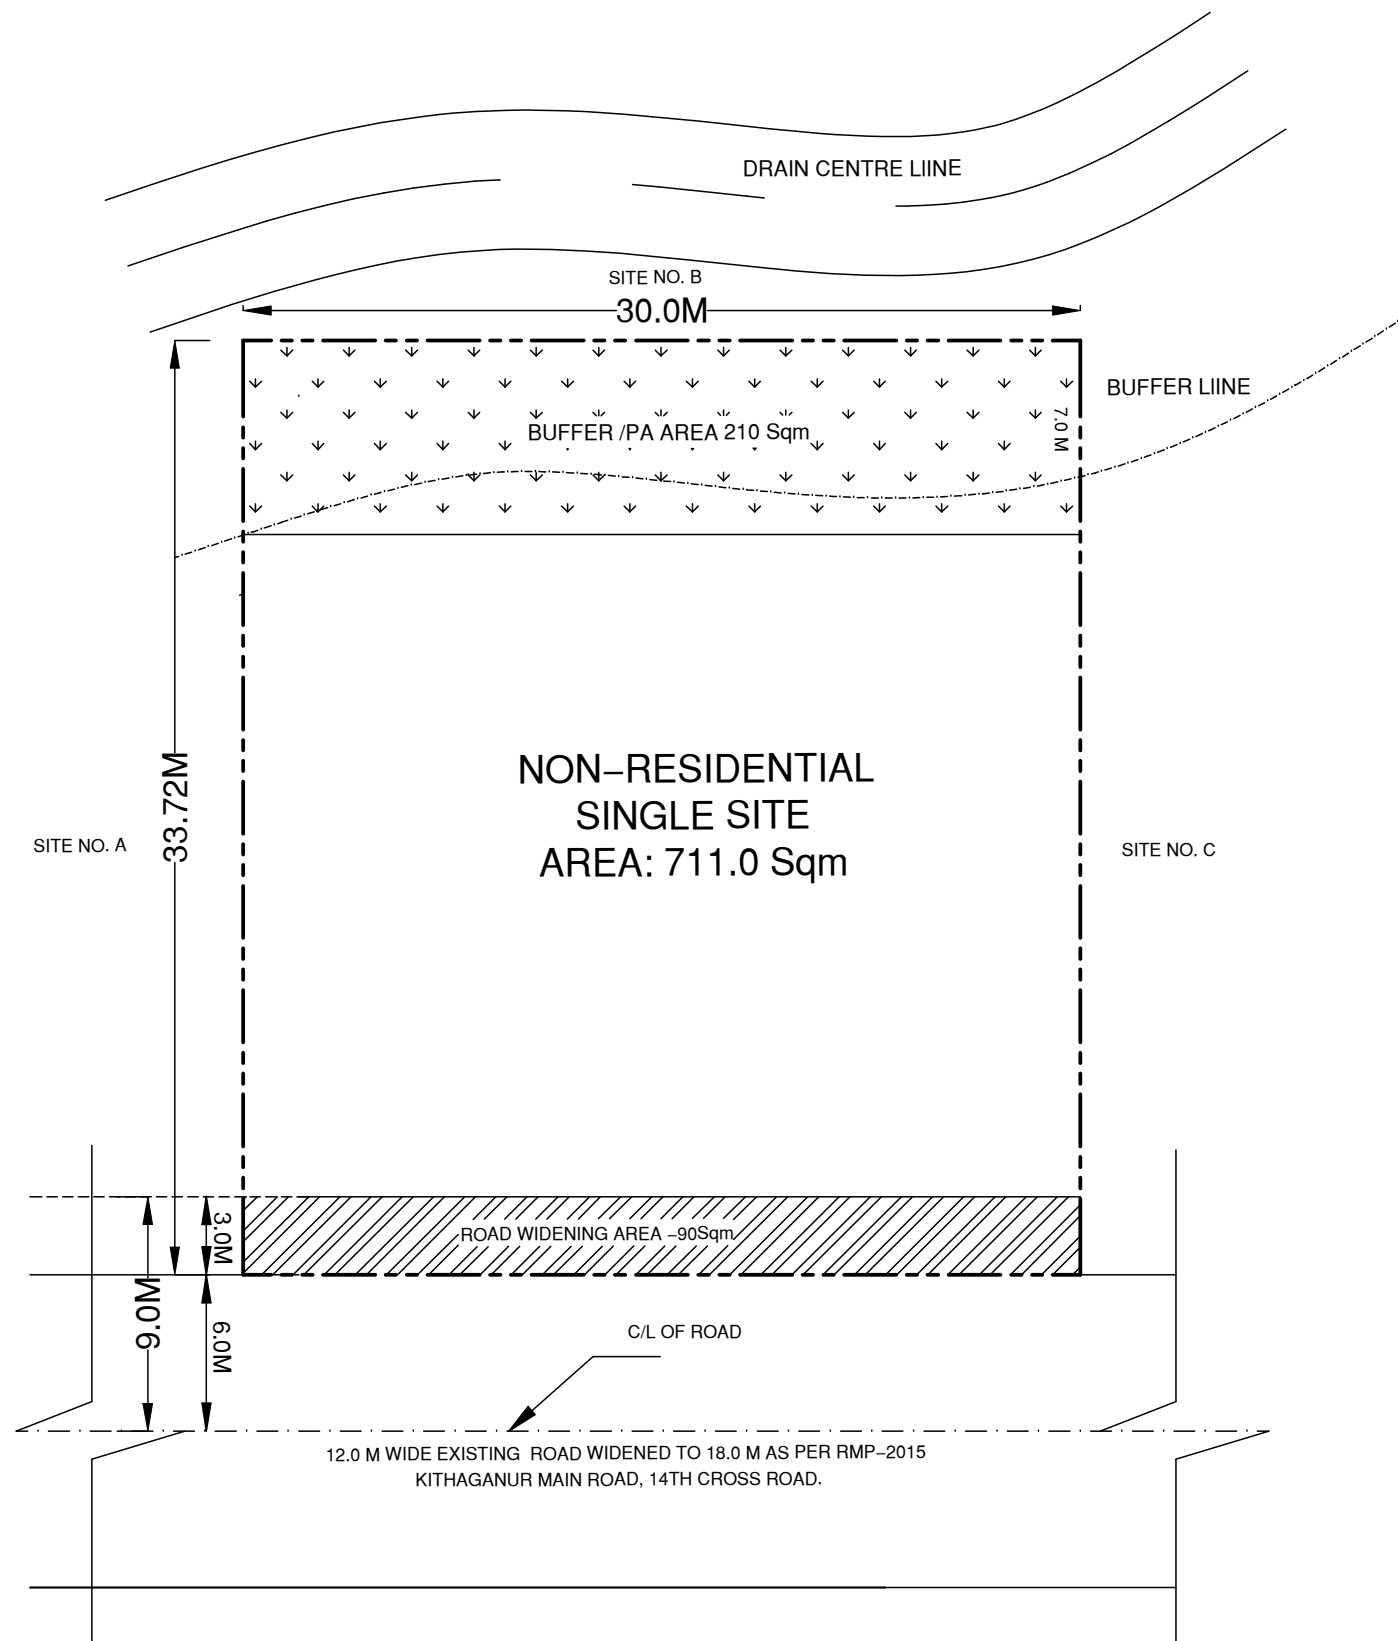

ADLR SKETCH SHOWING THE LOCATION OF THE PROPOSED SITE WITHIN THE SURVEY NUMBER.

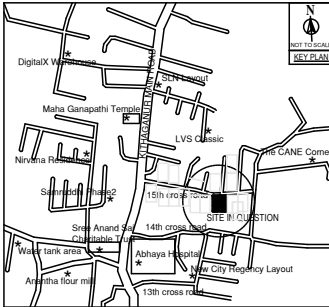KEY PLAN		CONVERSION ORDER DETAILS					
							
GENERAL CONDITIONS OF APPROVAL		LAND USE ANALYSIS			LEGEND		
1. The single plot layout plan is approved based on the survey sketch certified by the Assistant Director of Land records. 2. Building construction shall be undertaken only after obtaining approval for the building plan from the city corporation as per the approved single site layout plan. 3. The existing width of road abutting the site in question is marked in the plan. At the time of building plan approval the authority approving the building plan shall allow the maximum FAR permissible considering the minimum width of the road at any stretch towards any one side which shall join a road of equal or higher width. 4. The owner shall provide drinking water, waste water discharge system, solid waste management system and drainage system for the site in question. During the building plan approval the owner shall submit a design to implement the rain water harvesting to collect the rain water from the entire site area. 5. Approval of single site layout plan shall not be a document to claim title to the property. In case of pending cases under the Land Reforms Act/Section 136(3) of the Land Revenue Act, 1964, approval of single site layout plan shall be subject to final order. The applicant shall be bound by the final order of the court in this regard and in no case the fees paid for the approval of the single site layout plan will be refunded. 6. If it is found that the land proposed by the applicant includes any land belonging to the Government or any other private land, in such a case, the Authority reserves the rights to modify the single site layout plan or to withdraw the plan. 7. If it is proved that the applicant has provided any false documents or forged documents for the plan sanction, the plan sanction shall stand canceled automatically. 8. The applicant shall be bound to all subsequent orders and the decision relating to payment of fees as required by the Authority. 9. Adequate provisions shall be made to segregate wet waste, dry waste and plastics. Area should be reserved for composting of wet waste, dry waste etc. 10. No Objection Certificates/Approvals for the building plan should be obtained from the competent authorities prior to construction of building on the approved single site. 11. Sewage shall not be discharged into open spaces/vacant areas but should be reused for gardening, cleaning of common areas and various other uses. 12. If the owner wishes to modify the single site layout approval to multi-plot residential layout, the owner shall submit a request to the Greater Bengaluru Authority and obtain approval for the multi-plot residential layout plan as per the zoning regulations. 13. One tree for every 240.0 sq.m. of the total floor area shall be planted and nurtured at the site in question. 14. Prior permission should be obtained from the competent authority before constructing a culvert on the storm water drain between the land in question and the existing road attached to it if any. 15. To abide by such other conditions as may be imposed by the Authority from time to time.		SL. No	PARTICULARS	AREA IN Sqm.	%	--- -- PROPERTY BOUNDARY LINE ROAD WIDENING AREA PARK / OPEN SPACE --- -- BUFFER LINE --- -- BUFFER CENTRE LINE	
		1	NON-RESIDENTIAL AREA	711.70	70.35		
		2	ROAD WIDENING AREA	90.0	8.90		
		3	BUFFER / PARK AREA	210.0	20.75		
		4	TOTAL SITE AREA	1011.70	100.00		
		OWNER SIGNATURE		ARCHITECT SIGNATURE & REGISTRATION DETAILS			
		DRAWING TITLE			N All Dimensions in metres. SCALE 1:250		
		PLAN SHOWING THE NON - RESIDENTIAL SINGLE SITE LAYOUT FOR THE PROPERTY SITUATED IN SY.NO.****, **** VILLAGE, **** TALUK, BEARING KHATA/PID NO.***** , ***** CONSTITUENCY, BENGALURU ***** CORPORATION, BENGALURU.					
		SANCTIONING AUTHORITY					
NOTE							
1. The single plot plan is issued under The Provision of section 17 of KTCP Act 1961							
2. The applicant has Remitted Fees of Rs.***** vide challan No. ***** Dated : *.*.****							
3. The applicant has to abide by the conditions imposed in the single plot plan approval order							
4. This single plot plan issued vide number *****/**/*-***** dated : *.*.****							

SAMPLE FORMAT 30.0M x33.72 M SITE NON-RESIDENTIAL SINGLE PLOT LAYOUT PLAN

